




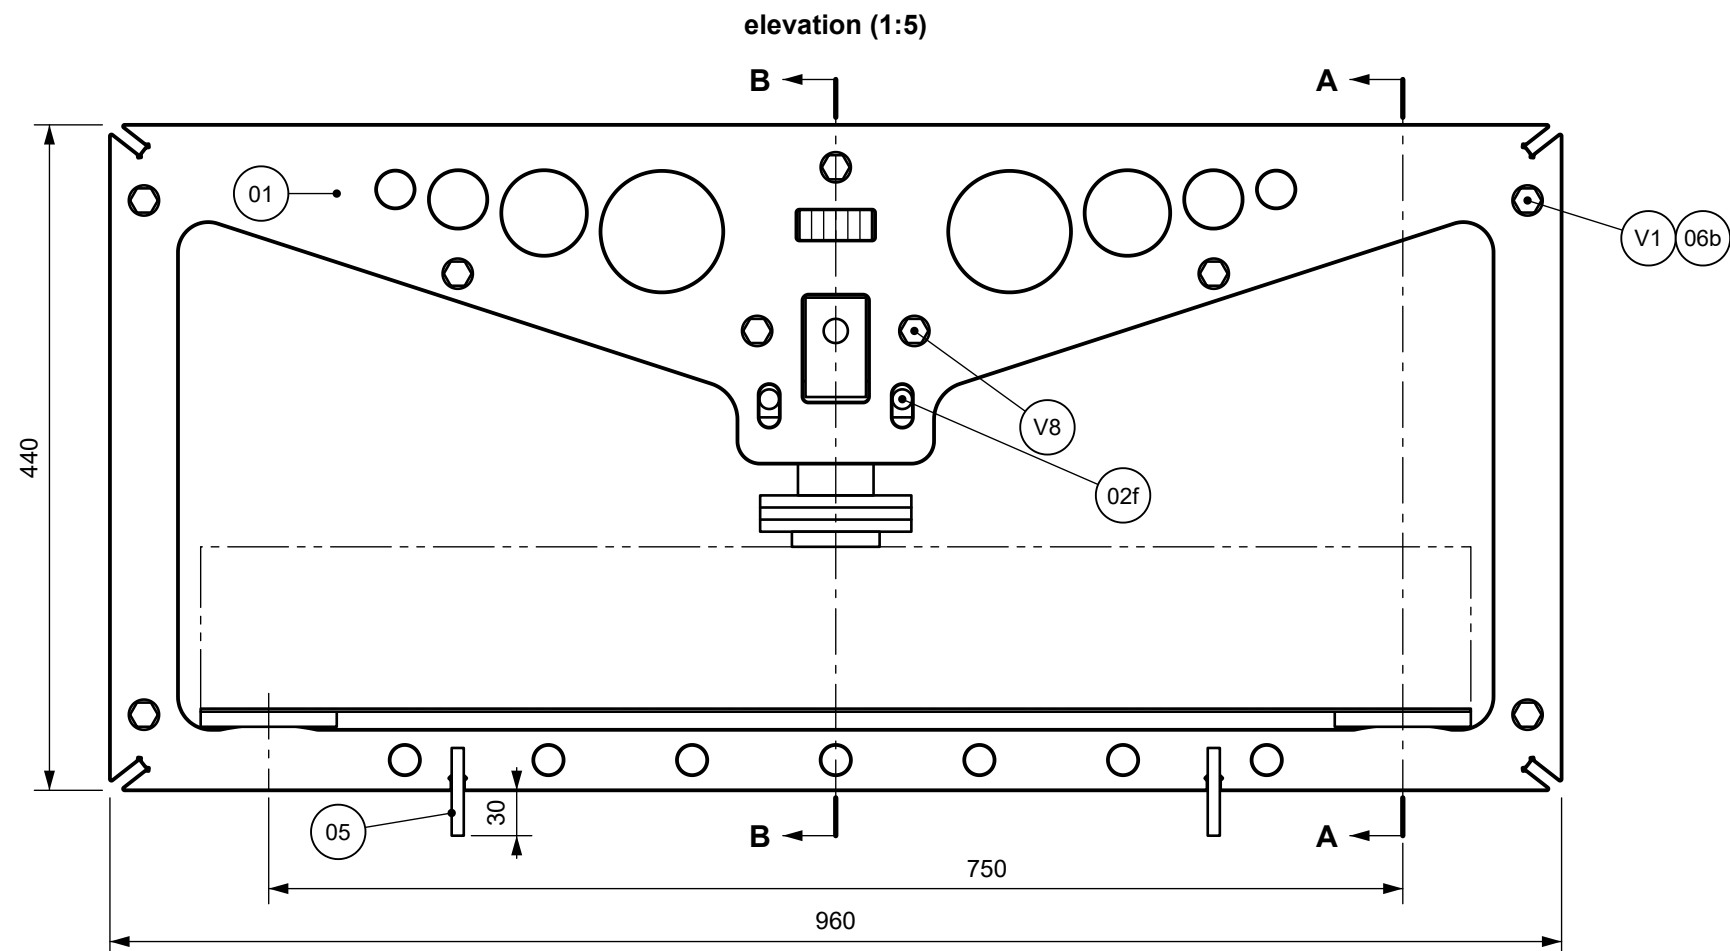

Les flancs portent SOUS les plats colles :
la face laterale de la poutre reste degaee.
Pieds 05, au-dela du plan, non figures.

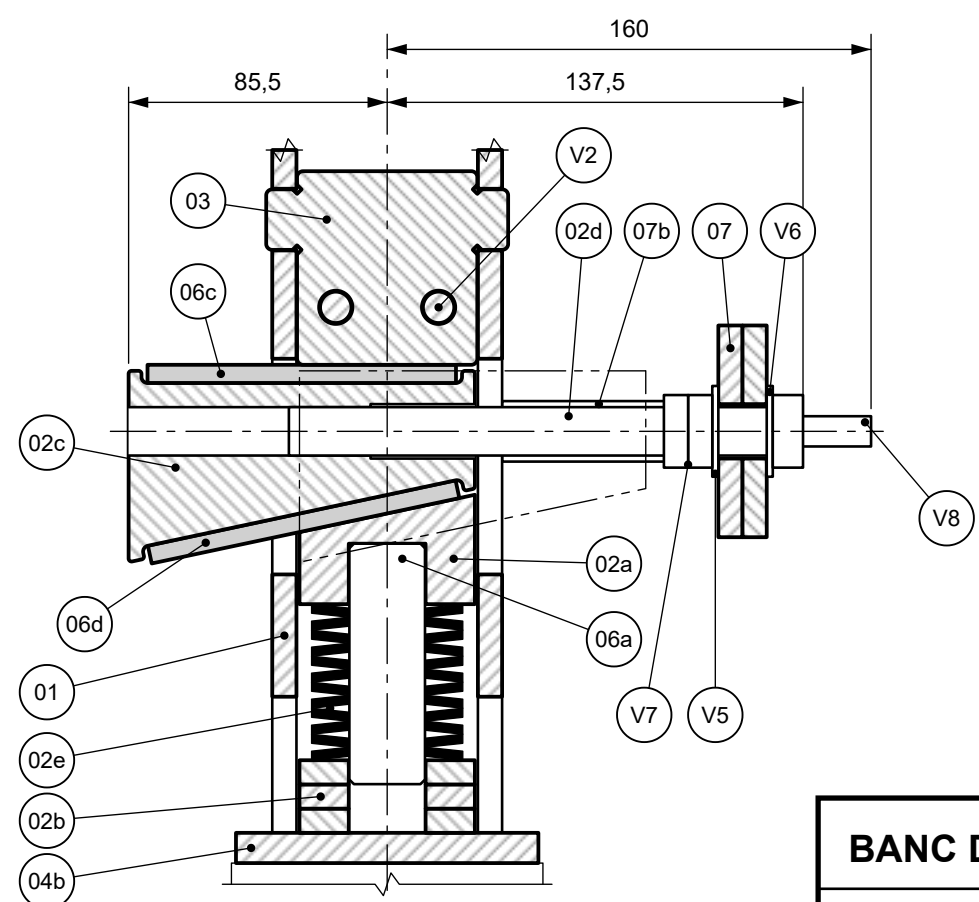

Le coin AVANCE VERS LA CHAPE en chargeant ; repousse vers son bout epais, il TIRE la vis vers l interieur :
la tete appuie, par deux rondelles trempees, sur la face exterieure des 2 platines ; monte a l envers, la vis ne retiendrait rien.
Douille sur la tete : 116,7 mm devant la tete de vis dans l etuve de 528,4, 10 de marge pour le decentrage du cadre.
En trait mixte a deux tirets, le coin 02c en fin de course : 56,5 depuis le repos.

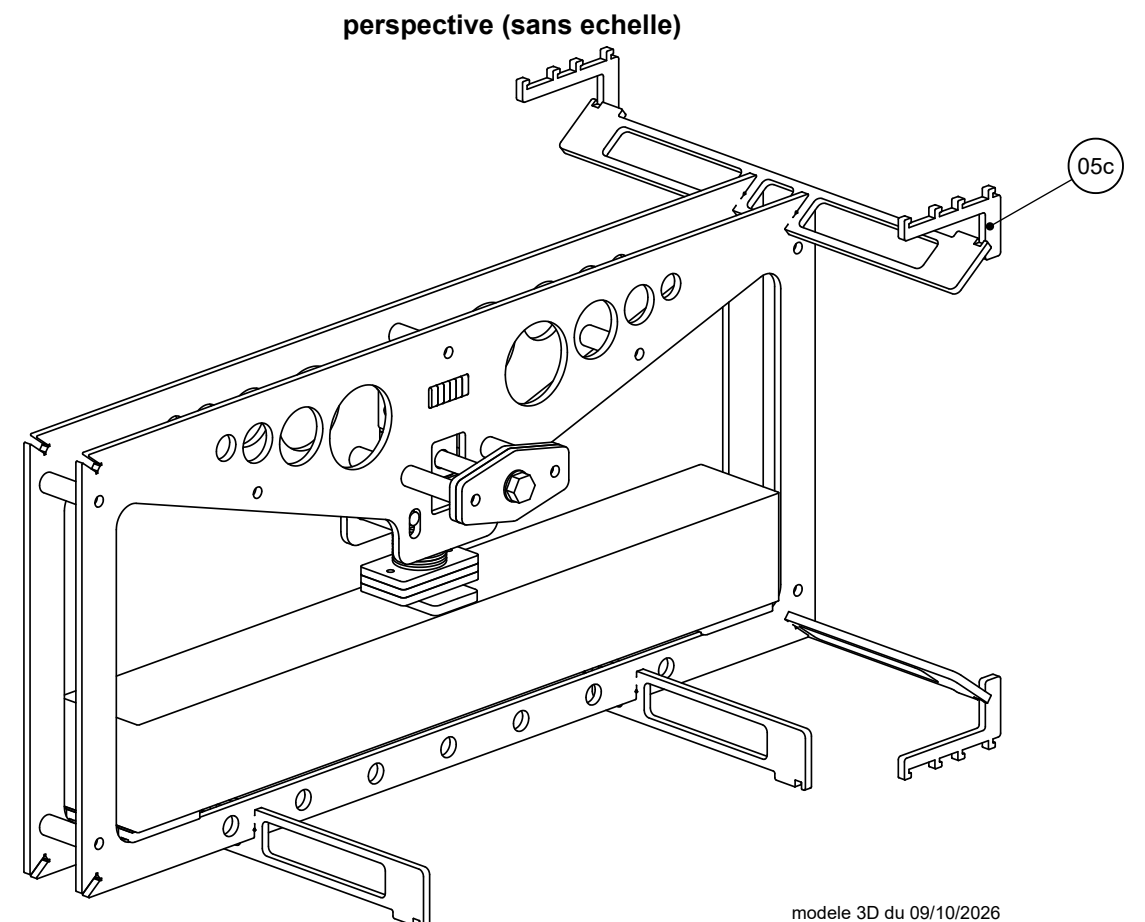

Pieds couches, pieds en V et crochets d etuve figures ensemble :
debout, les pieds couches restent sur la paillasse.

NIVEAUX (z depuis le chant bas des flancs)			
rep.	piece	z bas	z haut
03	traverse, 6 plaques	325,7	389,7
06c	plaque de frottement haute	319,7	325,7
02c	coin au repos, a y = 0	282,7	319,7
06d	plaque de frottement basse, y = 0	276,6	282,7
02a	coulisseau, a y = 0	246,6	276,6
06a	tourillon	187,1	266,6
02e	pile Belleville libre (+ cales V4)	195	246,6
02b	poussoir, 3 plateaux visses (V3)	171	195
04b	patin de charge	161	171
-	poutrelle (eprouvette)	54	161
04c	plats colles	52	54
04a	patins d appui, x = +/- 375	42	52
02d	vis M16 : axe	303,7	

Flexion 3 points, portee 750, capacite 12 kN.
Eprouvette : poutrelle 103 x 107 x 840, en trait mixte a deux tirets.
Pile Belleville, 12 rondelles EN 16983 A50 : 18,5 kN a plat, course 15,6 mm.
Lecture de charge : 9,65 mm de coulisseau a 12 kN.
Reglage par coin acier a 12 deg et vis M16 normale aux flancs :
0,425 mm de coulisseau et environ 549 N par tour de vis.
Hors tout couche sur pieds : 960 x 518,4 x 470 (x, y, z) ; flancs 76.
Debout dans l etuve : 969,5 de haut, 458,6 x 518,4 en plan ; etuve 538 x 528,4 x 1400.
Masse du cadre 34,5 kg. Reperes : NOMENCLATURE.md (Vn : visserie).

BANC DE FLEXION - ENSEMBLE		rep. 00	indice B 05/10/2026
matiere	brut	quantite	
voir nomenclature	-	1	
echelle	cotes en mm	banc de flexion	
1:5 sauf indication	tol. generale ISO 2768-m	poutrelle 103x107x840	